Deckenspiegel Erdgeschoss
Plan 530-521-1 + 530-521-2

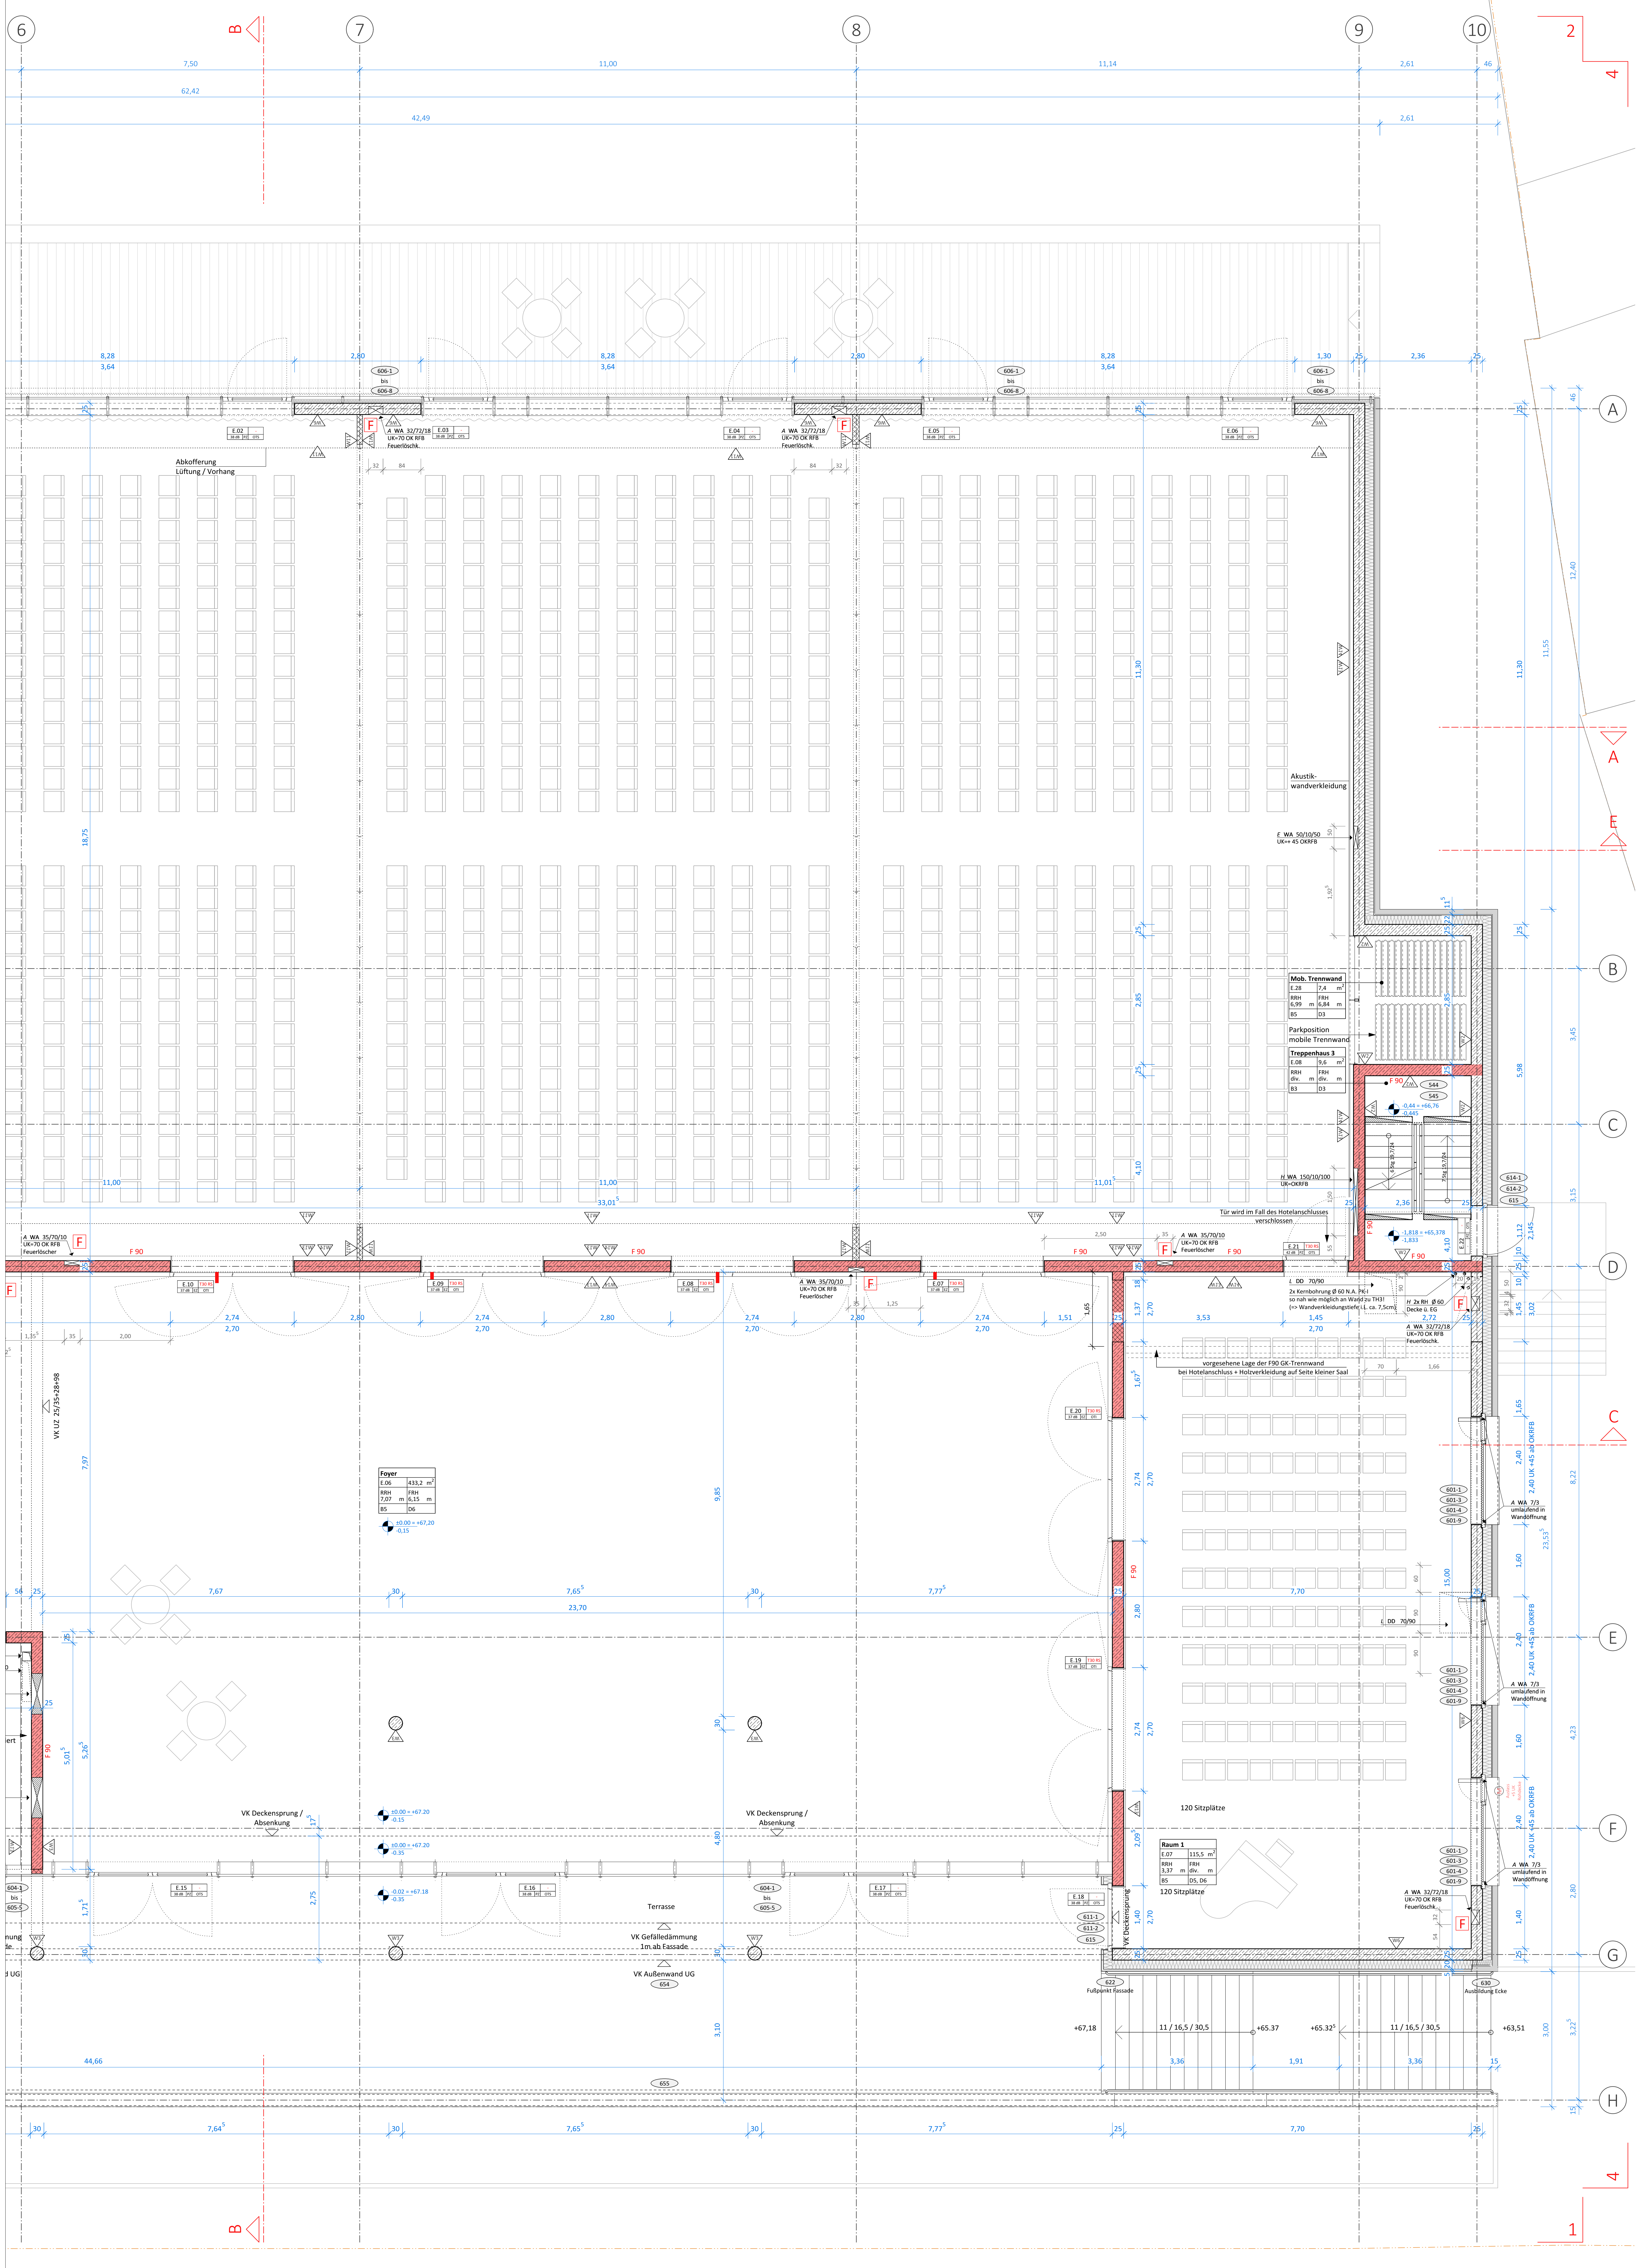
6
7
8
9
10
A
B
C
D
E
F
G
H
1
2
4
7,50
11,00
11,14
2,61
62,42
42,49
8,28
3,64
2,80
1,30
2,36
Abkofferung
Lüftung / Vorhang
Akustik-
wandverkleidung
Mob. Trennwand
E.28 7,4 m²
RRH 6,99 m
FRH 6,84 m
B5 D3
Parkposition
mobile Trennwand
Treppenhaus 3
E.08 9,6 m²
B3 D3
Tür wird im Fall des Hotelanschlusses verschlossen
vorgesehene Lage der F90 GK-Trennwand
bei Hotelanschluss + Holzverkleidung auf Seite kleiner Saal
F 90
F
Foyer
E.06 433,2 m²
RRH 7,07 m
FRH 6,15 m
B5 D6
Raum 1
E.07 115,5 m²
RRH 3,37 m
B5 D5, D6
120 Sitzplätze
Terrasse
VK Deckensprung /
Absenkung
VK Gefälledämmung
Im.ab Fassade
VK Außenwand UG
VK Deckensprung
Fußpunkt Fassade
Ausbildung Ecke
VK UZ 25/35+28+98
A WA 7/3
umlaufend in
Wandöffnung
2,40 UK +45 ab OKFFB
11 / 16,5 / 30,5
+67,18
+65,37
+63,51
44,66
23,70
13,01
11,00
7,67
7,65
7,77
7,70

LEGENDE STEMPEL

Raumstempel

Raumnummer	E.10	74,4 m²	
Raumbezeichnung	Windfang		
OKRFB bis UKRD	RRH 3,25 m	FRH 3,15 m	OKFFB bis UKFD
Oberflaeche Boden	B5	D10	Oberflaeche Decke

Türstempel

- Türnummer: T.01
- Brandschutz: T30
- Schallschutz: 32 dB
- Schließzylinder: PZ
- Obentürschließer: OTS

Oberflächen Wände

33 — Oberfläche Wand

LEGENDE OBERFLAECHEN

OBERFLAECHEN DECKE		OBERFLAECHEN BODEN	
D1	Beton, Roh	B1	Beton + Glattstrich
D2	Beton, Sicht	B2	Pflaster Tiefgarage
D3	Beton, gestrichen	B3	Estrich beschichtet
D4	Putz, gestrichen	B4	Kautschuk
D5	Abgeh. Decke GK, gestrichen	B5	Industrieparkett
D6	Abgeh. Decke GK, gelocht, gestr.	B6	Bühnenboden
D7	Innendämmung, gestrichen	B7	Bodenfliese
D8		B8	Betonwerkstein
D9		B9	Sauberlauf
D10		B10	einfacher Holzboden
D11		B11	OS-Beschichtung

OBERFLAECHEN WAENDE

W1	Beton ohne Anforderung	W9	Fliese
W2	Beton, gestrichen	W10	Abdichtung, Fliese
W3	Sichtbeton Betonplan	W11	Trockenbau, gestrichen
W4	Sichtbeton Brettschalung	W12	Trockenbau-Vorsatzschale
W5	Mauerwerk, gestrichen	W13	Holzverkleidung
W6	Putz, gestrichen	W14	Holzverkleidung Akustik
W7	Putz, Fliese	W15	Innendämmung, gestrichen
W8	Putz, Abdichtung, Fliese	W16	

LEGENDE ABKÜRZUNGEN

AK	Außenkante	RH	Rohrhülse
AS	Anschlagschiene	RR	Regenrohr (Fallrohr)
BRH	Brüstungshöhe über RFB	S	Sanitärinstallation
DA	Deckenaussparung	SWS	Senkrechter Wandschlitz
DD	Deckendurchbruch	T30/90	Brandschutztür
DS	Deckenspung	Tds	Türe dicht-, selbstschließend
E	Elektroinstallation	Td	Türe dichtschließend
F30/90	Brandschutzverglasung	TS	Trennschiene
FD	Fußbodendurchbruch	UK	Unterkante
FFB	Fertigfußboden	VK	Vorderkante
FK	Fußbodenkanal	VKB	Vorderkanten Bodenplatte
FS	Fußbodensprung	VKD	Vorderkante Decke
H	Heizungsinstallation	VM	Vormauerung
HG	Hausgrund	WA	Wandaussparung
L	Lüftungsinstallation	WD	Wärmedämmung
LBS	Lüftungsbaustein	WWS	Waagrechter Wandschlitz
OK	Oberkante		
OKFFB	Oberkante Fertigfußboden		
OKRFB	Oberkante Rohfußboden		
RDS	Rohdeckensprung		

LEGENDE ZEICHNUNG

▨	Stahlbeton	▭	BS Bodenschlitz
🟥	Stahlbeton Brandschutz	⬚	DD Deckendurchbruch
▨	WU-Beton	▨	FD Fußbodendurchbruch
▦	Betonfertigteil	☒	WS Wandschlitz
▨	Mauerwerk	☒	WD Wanddurchbruch
🟥	Mauerwerk Brandschutz		
▦	Trennwand Trockenbau		
🟥	Trennwand TB. Brandschutz	+ 2.82 / + 2.70	OKFFB / OKRFB
☒	Installations-Systemwand	580	siehe Detailplan 580
▨	Dämmung		

BRÜSTUNGSHÖHEN UND TÜRHÖHEN AB OK RFB!

SCHACHTABMAUERUNGEN ERST NACH AUFFORDERUNG
DURCH DIE BAULEITUNG SCHLIESSEN BEPLANKUNGEN
STÄNDERWÄNDE ERST NACH INSTALLATION HLS!

INDEX	DATUM	ART DER ÄNDERUNG	VON
A	16.11.15	Detailverweise, Div. Rohbau, Planfreigabe	HT
B	11.1.16	Fassadenecke Achsen 10/G, Anpassung Anschluss Hotel	HT
C	17.3.16	Div. Anpassung Rohbau	HT
D	23.6.16	Anpassungen SD-Planung N.A. HLS und ELT	HT
E	1.9.16	Anpassungen Stützwand / Anschlusshöhen	HT
H	5.7.17	Übernahme Index EG Plan 1, Planstand Dokumentation	HT

SÄMTLICHE MASSE SIND VOM UNTERNEHMER AM BAU
VERANTWORTLICH ZU PRÜFEN!

PLANNUMMER 530-502-2

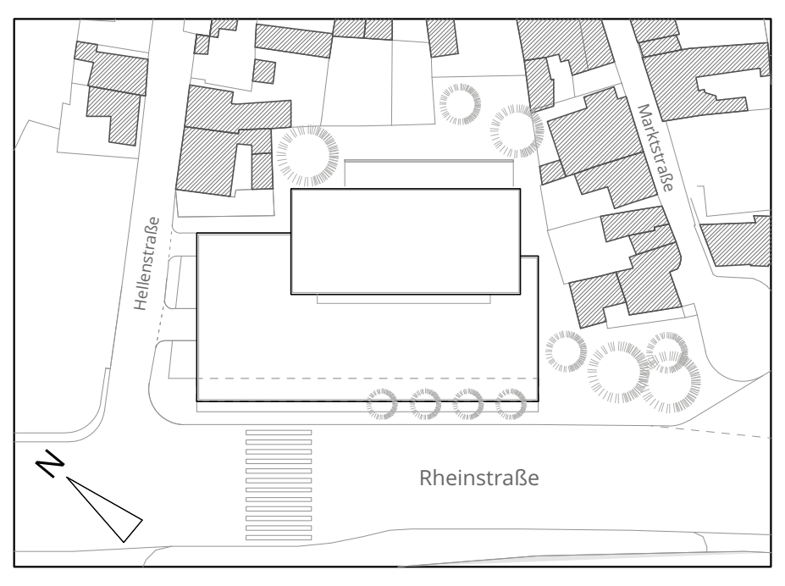
Marktstraße
Hellenstraße
Rheinstraße
N

WERKPLANUNG

BAUVORHABEN

Stadt- & Kongresshalle Vallendar
Rheinstrasse | 56179 Vallendar

BAUHERR

Stadt Vallendar

Rathausplatz 5 | 56179 Vallendar
T +49 (0)261 - 66 75 - 180
F +49 (0)261 - 66 75 - 7814

ARCHITEKT

DREI ARCHITEKTEN
Haag · Haffner · Konsek · Streule · Vogel

Rotebühlstrasse 87 | 70178 Stuttgart
T +49 (0)711 - 66 99 5 - 0
F +49 (0)711 - 66 99 5 - 50
mail@drei-architekten.de

PLANINHALT

Erdgeschoss
Plan 2 - Süd-Ost

DATUM	20.04.15	LEISTUNGSPHASE	WERKPLANUNG
DRUCK	5.7.17	INDEX	H
PLANGRÖSSE	A0	PLANNUMMER	530-502-2
MASSSTAB	1:50		
GEZEICHNET	HT		
GEPRÜFT			