
Deckenspiegel Obergeschoss
Plan 530-522-1 + 530-522-2

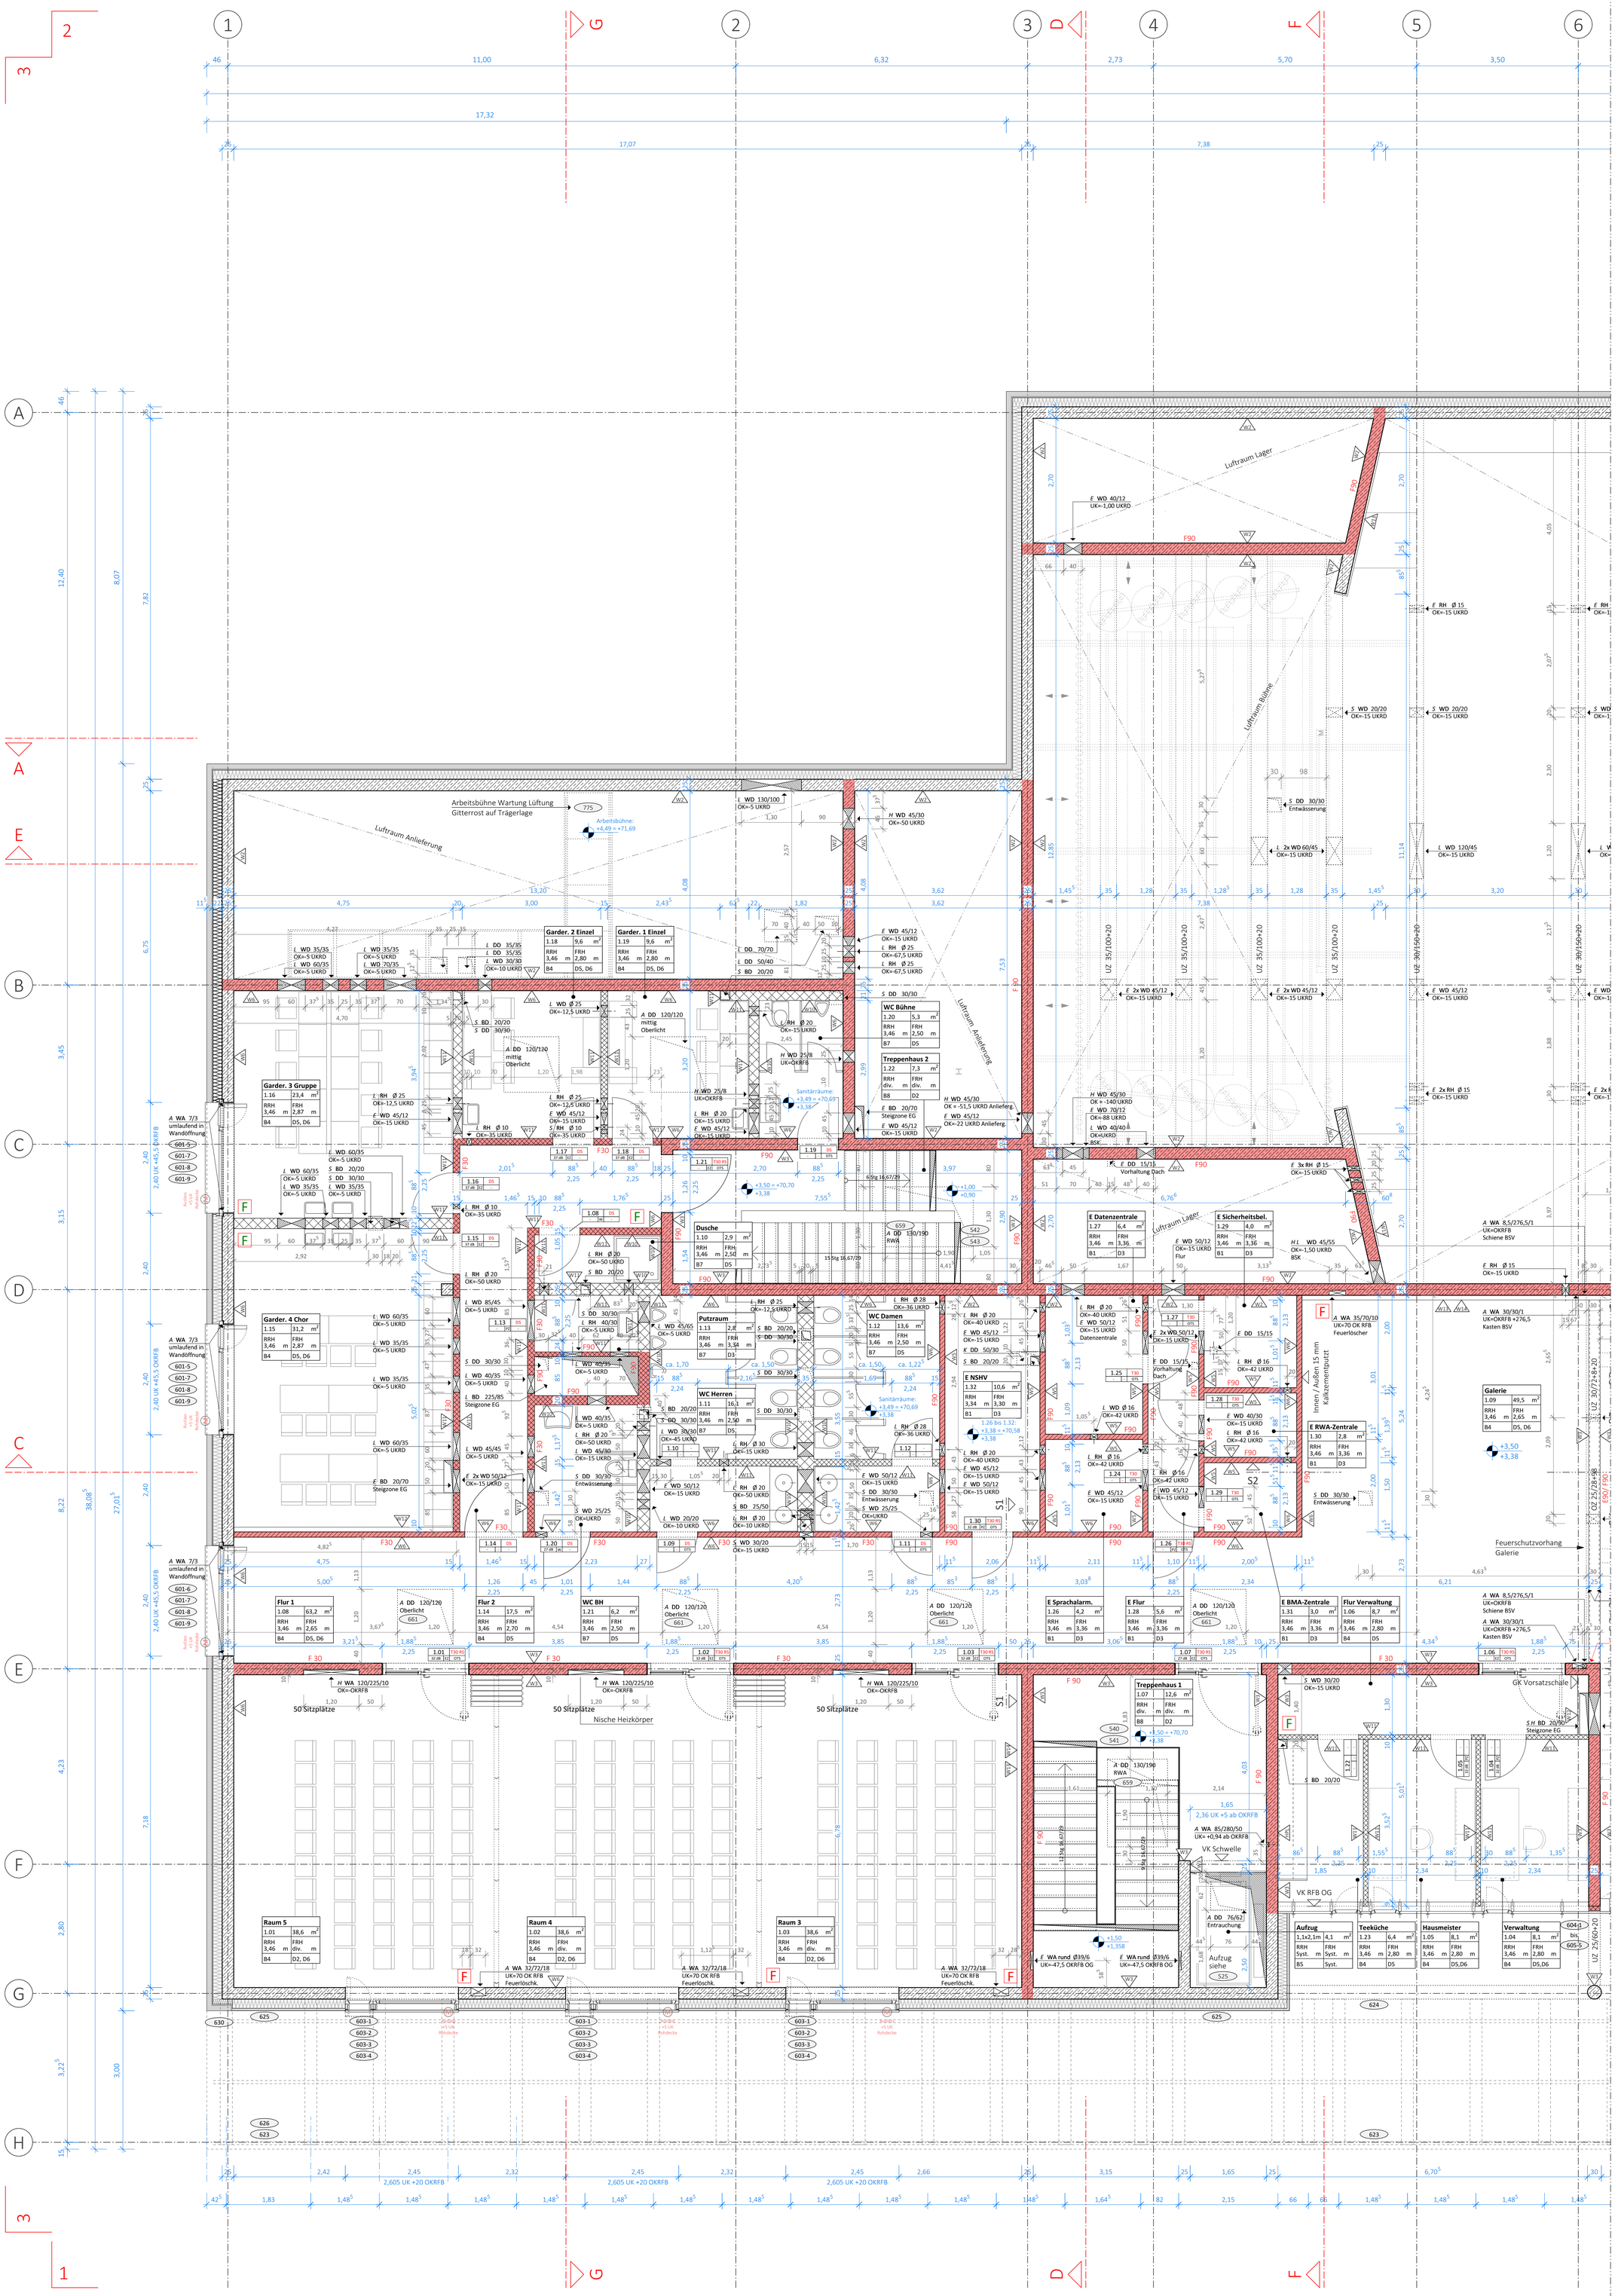

LEGENDE STEMPEL

Raumstempel

Windfang			Raumbezeichnung
E.10	74,4 m²		
RRH 3,25 m	FRH 3,15 m		
B5	D10		Oberflaeche Decke

Raumnummer · OKRFB bis UKRD · Oberflaeche Boden · OKFFB bis UKFD

Türstempel

T.01 | T30 | 32 dB | EI2 | 075

Türnummer · Schallschutz · Schließzylinder · Brandschutz · Obentürschließer

Oberflächen Wände

33 — Oberfläche Wand

LEGENDE OBERFLAECHEN

OBERFLAECHEN DECKE

D1 Beton, Roh
D2 Beton, Sicht
D3 Beton, gestrichen
D4 Putz, gestrichen
D5 Abgeh. Decke GK, gestrichen
D6 Abgeh. Decke GK, gelocht, gestr.
D7 Innendämmung, gestrichen
D8
D9
D10
D11

OBERFLAECHEN BODEN

B1 Beton + Glattstrich
B2 Pflaster Tiefgarage
B3 Estrich beschichtet
B4 Kautschuk
B5 Industrieparkett
B6 Bühnenboden
B7 Bodenfliese
B8 Betonwerkstein
B9 Sauberlauf
B10 einfacher Holzboden
B11 OS-Beschichtung

OBERFLAECHEN WAENDE

W1 Beton ohne Anforderung
W2 Beton, gestrichen
W3 Sichtbeton Betonplan
W4 Sichtbeton Brettschalung
W5 Mauerwerk, gestrichen
W6 Putz, gestrichen
W7 Putz, Fliese
W8 Putz, Abdichtung, Fliese
W9 Fliese
W10 Abdichtung, Fliese
W11 Trockenbau, gestrichen
W12 Trockenbau-Vorsatzschale
W13 Holzverkleidung
W14 Holzverkleidung Akustik
W15 Innendämmung, gestrichen
W16

LEGENDE ABKÜRZUNGEN

AK Außenkante
AS Anschlagschiene
BRH Brüstungshöhe über RFB
DA Deckenaussparung
DD Deckendurchbruch
DS Deckensprung
E Elektroinstallation
F30/90 Brandschutzverglasung
FD Fußbodendurchbruch
FFB Fertigfußboden
FK Fußbodenkante
FS Fußbodensprung
H Heizungsinstallation
HG Hausgrund
L Lüftungsinstallation
LBS Lüftungsbaustein
OK Oberkante
OKFFB Oberkante Fertigfußboden
OKRFB Oberkante Rohfußboden
RDS Rohdeckensprung
RH Rohrhülse
RR Regenrohr (Fallrohr)
S Sanitärinstallation
SWS Senkrechter Wandschlitz
T30/90 Brandschutztür
TS Türe dicht-, selbstschließend
Td Türe dichtschließend
TS Trennschiene
UK Unterkante
VK Vorderkante
VKD Vorderkante Decke
VM Vormauerung
WA Wandaussparung
WD Wärmedämmung
WWS Waagrechter Wandschlitz

LEGENDE ZEICHNUNG

Stahlbeton · Stahlbeton Brandschutz · WU-Beton · Betonfertigteil · Mauerwerk · Mauerwerk Brandschutz · Trennwand Trockenbau · Trennwand TB. Brandschutz · Installations-Systemwand · Dämmung

BS Bodenschlitz · DD Deckendurchbruch · FD Fußbodendurchbruch · WS Wandschlitz · WD Wanddurchbruch

+2.82 / +2.70 OKFFB / OKRFB

580 — siehe Detailplan 580

BRÜSTUNGSHÖHEN UND TÜRHÖHEN AB OK RFB!

SCHACHTABMAUERUNGEN ERST NACH AUFFORDERUNG DURCH DIE BAULEITUNG SCHLIESSEN BEPLANKUNGEN STÄNDERWÄNDE ERST NACH INSTALLATION HLS!

INDEX	DATUM	ART DER ÄNDERUNG	VON
A	16.11.15	Detailverweise, Div. Rohbau, Planfreigabe	HT
B	11.1.16	Fassadenecke + Erw. Vordach, Anpassung N.A Aufzugsbauer	HT
C	17.3.16	Schallschutz Türen, Detailverweise	HT
		Anpassung Installationswände und Türen Sanitärräume	HT
D	23.6.16	Überarbeitung Küche und WCs entspr. Fliesenspiegel,	HT
		Aussparungen Führungsschienen Feuerschutzvorhang	
E	5.7.17	Planstand Dokumentation	HT

SÄMTLICHE MASSE SIND VOM UNTERNEHMER AM BAU VERANTWORTLICH ZU PRÜFEN!

PLANNUMMER 530-503-1

WERKPLANUNG

BAUVORHABEN

Stadt- & Kongresshalle Vallendar
Rheinstrasse | 56179 Vallendar

BAUHERR

Stadt Vallendar

Rathausplatz 5 | 56179 Vallendar
T +49 (0)261 - 66 75 - 180
F +49 (0)261 - 66 75 - 7814

ARCHITEKT

DREI ARCHITEKTEN
Haag · Haffner · Konsek · Streule · Vogel

Rotebühlstrasse 87 | 70178 Stuttgart
T +49 (0)711 - 66 99 5 - 0
F +49 (0)711 - 66 99 5 - 50
mail@drei-architekten.de

PLANINHALT

Obergeschoss
Plan 1 - Nord-West

DATUM	20.04.15	LEISTUNGSPHASE	WERKPLANUNG
DRUCK	5.7.17	INDEX	E
PLANGRÖSSE	A0	PLANNUMMER	
MASSSTAB	1:50		
GEZEICHNET	HT		
GEPRÜFT			530-503-1