KONGRESSHALLE VALLENDAR

STÄDTEBAULICHE INTEGRATION

Das Gebäude folgt dem Verlauf der Rheinstrasse und orientiert sich an der vorhandene Struktur. Der ablesbare Saal reagiert auf die umgebende kleinteiligere Bebauung. Die zum Rhein orientierte Erschließungsspange mit auskragendem Dach betont den Eingangsbereich am Rhein.

ERSCHLIESSUNG UND NUTZUNGSVERTEILUNG

Über die vorgelagerte Freitreppe wird der zentral angeordnete Haupteingang erreicht. Hier gelangt der Besucher über das zentrale Foyer zu den Sälen. Diese können zu einem gemeinsamen großen Raum zusammengeschaltet werden. Neben dem Haupteingang liegt einer der Vereinsräume, der zusammen mit dem Küchenbereich genutzt werden kann. Die Anlieferung zur Küche und zum Saal erfolgt über einen gemeinsamen Anlieferbereich. Hier ist auch die Erschließungstreppe Bühne - Küche - Garderoben angeordnet, welche die drei Bereiche auf kurzem Weg miteinander verbindet. Über das Haupttreppenhaus kann das Obergeschoss mit den dort vorhandenen weiteren Vereinsräumen und Verwaltungsbereich erreicht werden. Die drei Vereinsräume können zu einem großen Raum zusammengeschaltet werden. Eine zum Foyer gerichtete Galerie verbindet Erd- mit Obergeschoss. Auf beiden Ebenen verteilt wurden die WC-Anlagen, um sowohl die Saal- als auch Vereinsnutzung gleichzeitig zu ermöglichen. Im Untergeschoss befindet sich die ebenerdig erreichbare Tiefgarage, diese ist über den Aufzug barrierefrei mit den anderen Geschossen verbunden.

KONSTRUKTION, MATERIAL, ÄUSSERES ERSCHEINUNGSBILD

Der Entwurf basiert auf einem klaren Grundrisslayout, welches sich in der Materialität widerspiegelt. Wände und Decken aus Stahlbeton bilden die Grundstruktur für das Gebäude. Im Inneren sind Wände und teilweise Decken in Sichtbetonflächen ausgeführt. Leichte Trennwände sind in Gipskarton erstellt. Zusammen mit Holzakustikverkleidungen im Foyer und den Sälen und Holzeinbauten wird das Erscheinungsbild aufgewertet. Saal, Foyer und Vereinsräume sind mit gerauchtem Parkett ausgeführt. In den übrigen Flächen sind Bodenbeläge aus Linoleum (Flure, Garderobe, Verwaltung) und Feinsteinzeug (WC, Küche) angedacht. Decken sind in weiten Bereichen mit Akustikverkleidungen aus Gipskarton ausgeführt. Alle Öffnungen als 3-fach verglaste Pfostenriegelfassaden in Holz mit äußeren Alu-Deckschalen. Die Tiefgarage ist mit einer dauerhaften Kunstoffbeschichtung, welche sich leicht reinigen lässt, versehen.

Außen wird eine dauerhafte Fassadenverkleidung vorgeschlagen. Alle wesentlichen Flächen sind in großformatigen durchgefärbten Betonwerksteinverkleidungen gedacht, Rücksprünge als hinterlüftetete Fassade mit großformatiger Faserzementverkleidung in unterschiedlichen Formaten. Diese kann in verschiedenen Oberflächen (geschliffen, gestrahlt, gebürstet) ausgeführt werden, um eine plastischere Wirkung zu erzielen. In die Rücksprünge integriert sind die Pfosten-Riegel-Fassaden.


HAUSTECHNIK UND ENERGIEKONZEPT

Der Neubau hat eine kompakte Bauform mit hoher Dämmstoffstärke. Die Unterseite der Geschossdecke zwischen Erd- und Untergeschoss ist ebenfalls gedämmt. Alle technischen Betriebsräume sind wegen der Hochwassergefahr im Obergeschoss angeordnet, was kurze Wege im Gebäude ermöglicht. Hausanschluss und Transformatorraum sind im Erdgeschoss von außen erreichbar. Die Lüftungszentrale wurde in 2 separat nutzbare Teile gesplittet, wobei die eine Anlage dem großen Saal, Foyer und großem Vereinsraum zugeordnet ist, währrend die andere Anlage die Küche, Bühne und die übrigen Vereinsräume versorgt. Die restlichen Technikräume befinden sich als große Einheit über dem Vereinsraum und sind separat erreichbar. Auf dem Hallendach ist eine PV-Anlage zur Eigennutzung gedacht. Das auf den Dächern anfallende Regenwasser wird in den WC-Anlagen weitergenutzt.

MASSNAHMEN ZUR REDUZIERUNG DER FOLGEKOSTEN

Dauerhafte Materialien wie Sichtbeton im Innenbereich, geöltes Parkett in den Sälen und teilweise Wandverkleidungen aus Holz reduziert zusammen mit dem dezentralen teilbaren Lüftungskonzept die Folgekosten. Eine PV-Anlage für die Eigenversorgung und Grauwassernutzung tragen weiter zur Wirtschaftlichkeit bei. Auch an den Fassaden sind dauerhafte Materialien wie Betonwerkstein und Faserbeton eingesetzt.


ERDGESCHOSS

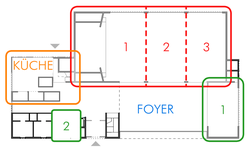

Erdgeschoss

- Zentrale Lage des Foyers zu den einzelnen Sälen und zum grossen Vereinsraum
- Kleiner Vereinsraum einzeln nutzbar
- Küche an Anlieferungshof angeschlossen und räumlich von den übrigen Nutzungen getrennt


EVENTNUTZUNG / AUSSENBEZUG

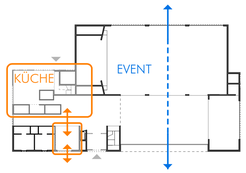

Eventnutzung und Aussenbezug

- Zusammenschaltbarkeit der Säale 1 2 3 und des grossen Vereinsraumes mit dem Foyer zu einer Eventfläche
- Durchnutzung möglich
- Nutzung des kleinen Vereinsraumes für die Küche mit Aussenbezug
- zentrale Lage der Küche zu Eventfläche und zusätzlicher Anrichte

OBERGESCHOSS

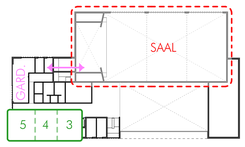


Obergeschoss

- Garderoben separat zugänglich angeordnet, Bezug zum Saal
- Vereinsräume 3 4 5 sind zu einem grossen Saal zusammenschaltbar und liegen an der gemeinsamen Galerie zum Foyer




LAGEPLAN 1|500


ERDGESCHOSS 1|200

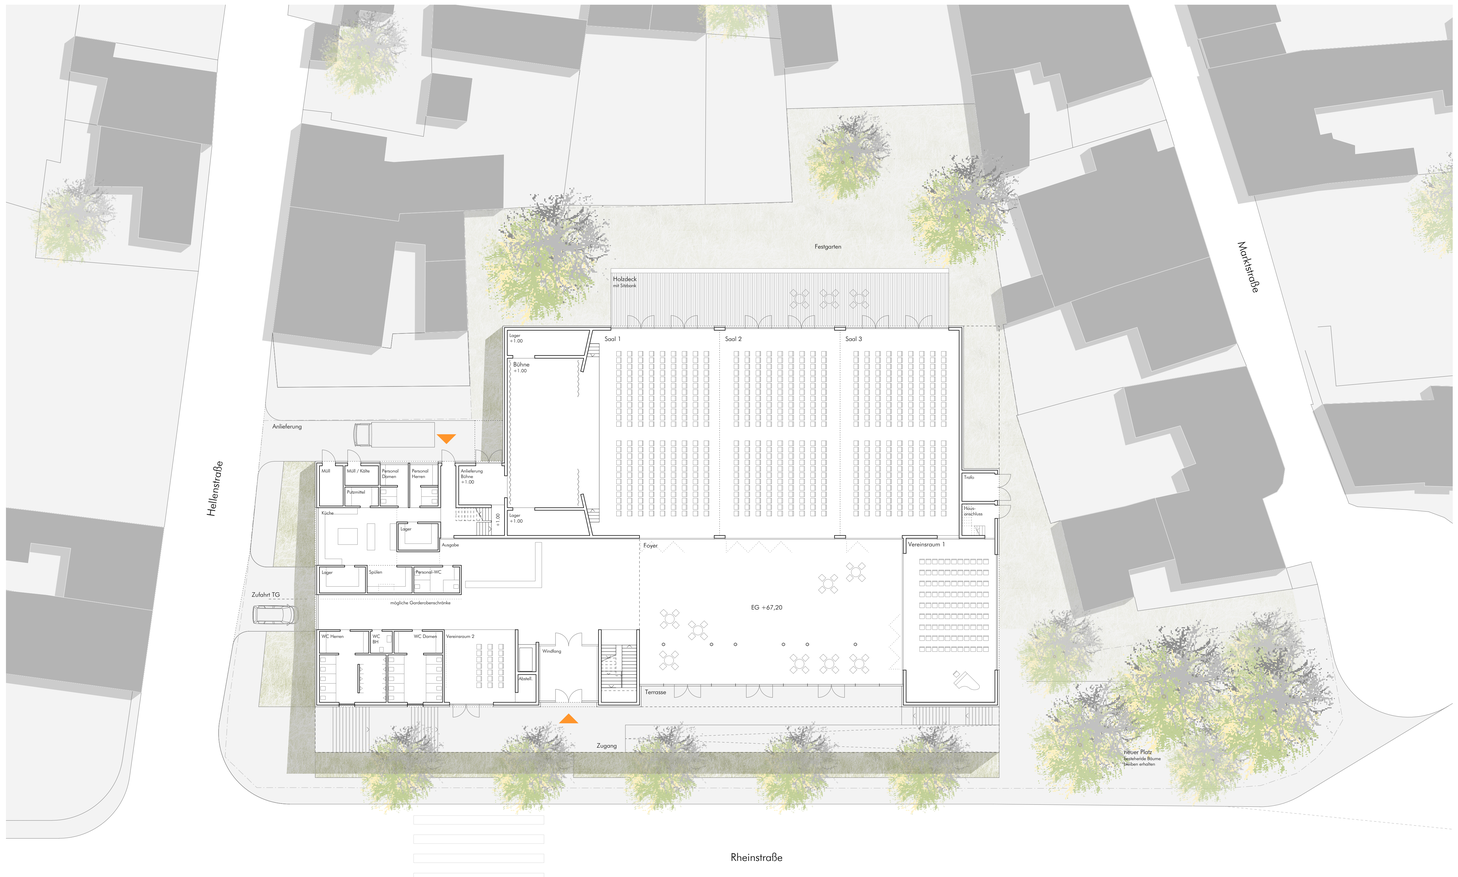

ANSICHT RHEINSTRASSE 1|200

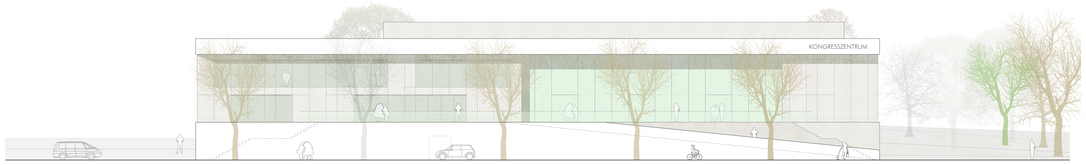

ANSICHT GARTEN 1|200

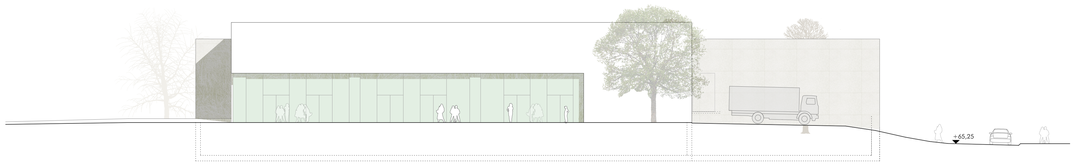

SCHNITT SAAL 1|200

