

OBERGESCHOSS 1|200

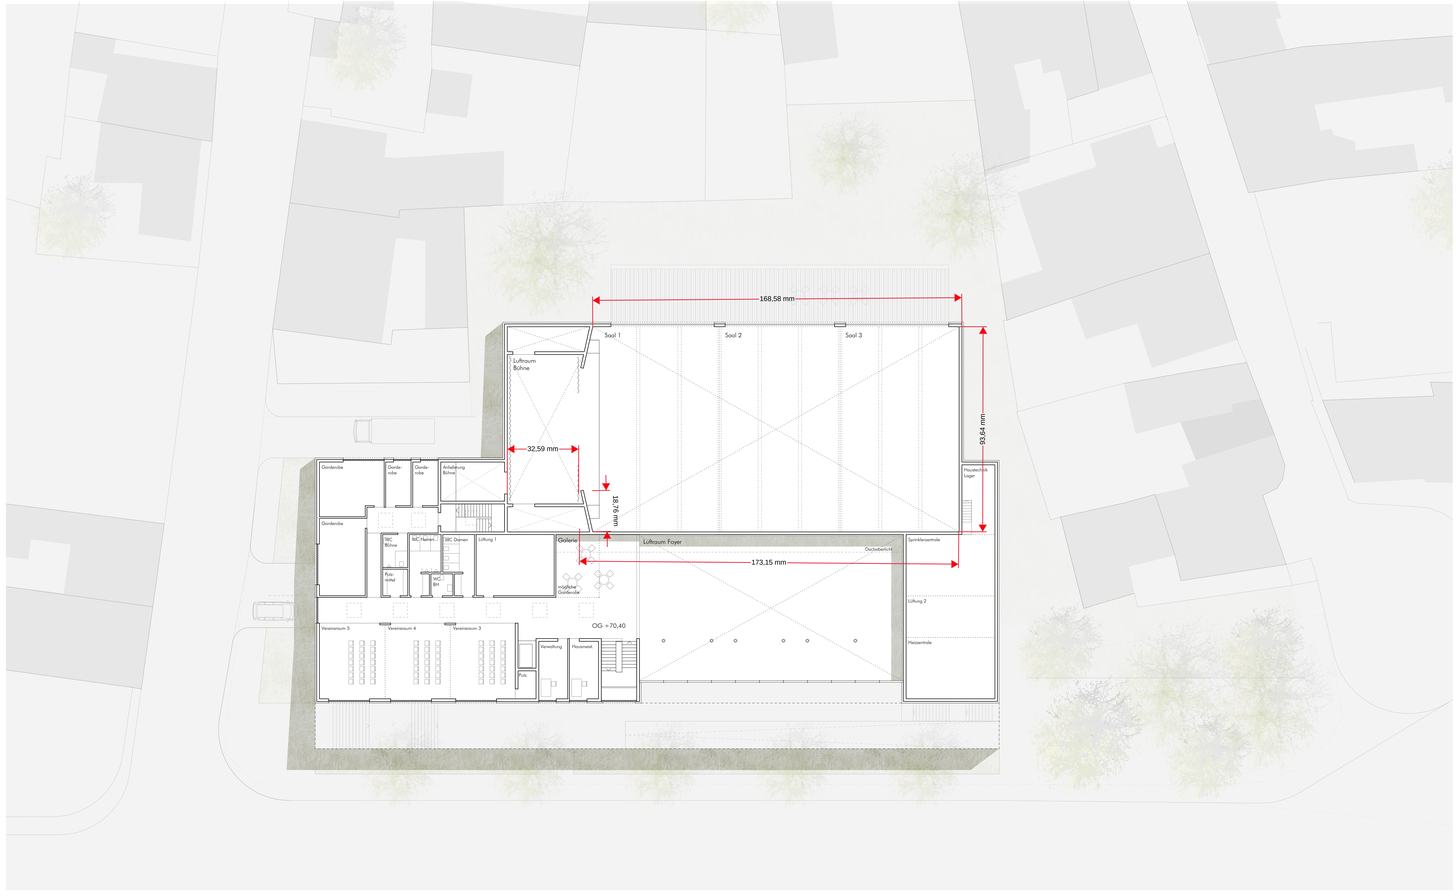


ANSICHT MARKTSTRASSE 1|200

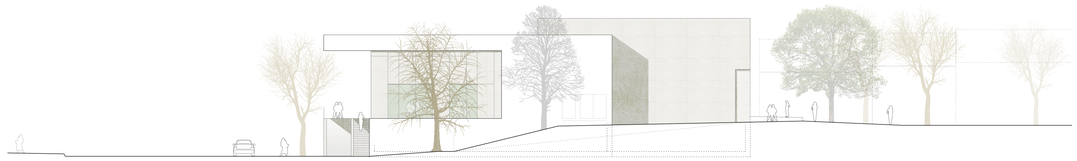


ANSICHT HELLENSTRASSE 1|200




SCHNITT SAAL-FOYER 1|200

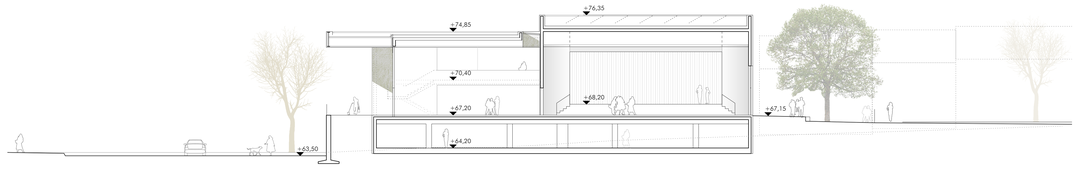

UNTERGESCHOSS 1|200

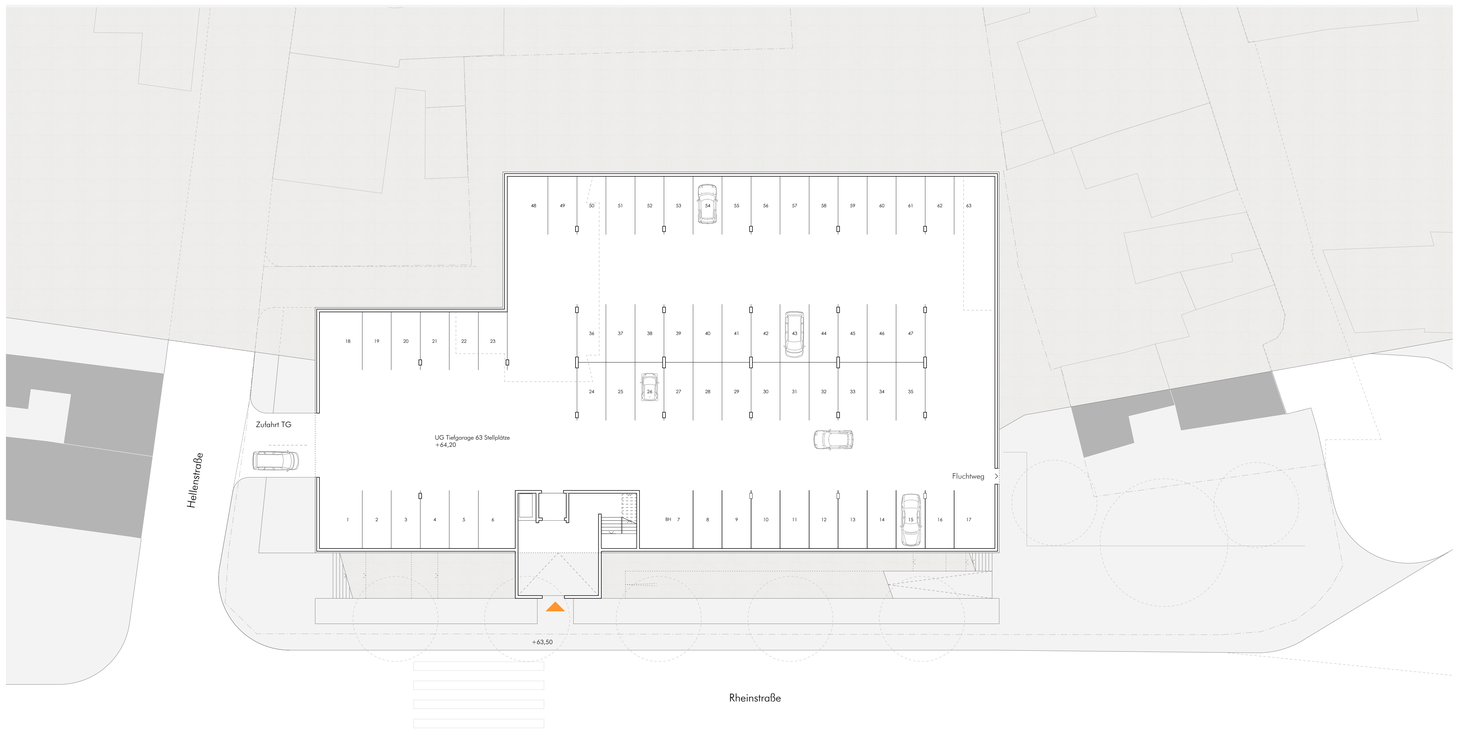

FASSADENSCHNITT 1|50

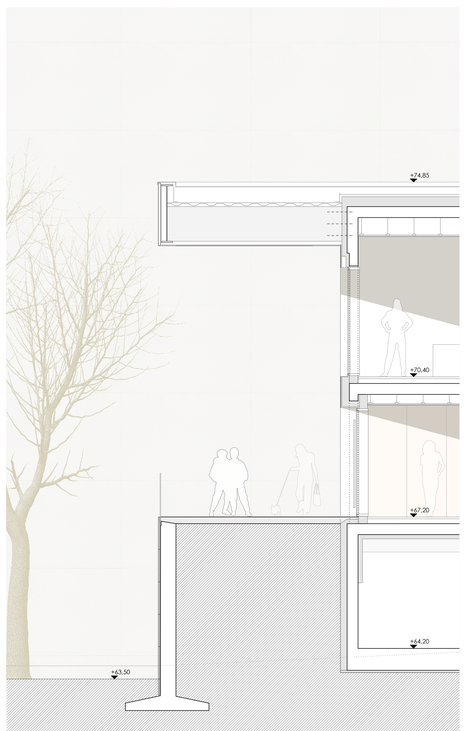

KONSTRUKTION UND MATERIAL

DACH
- Dachbegrünung extensiv oder PV-Anlage (Halle)
- Wärmedämmung
- Stahlbetondecke
- abgehängte Decke

AUSSENWAND
- Stahlbetonwand in Ortbeton
- Wärmedämmung Mineralwolle
- Faserbetonverkleidung in Rücksprüngen bzw. Betonwerksteinverkleidung an übrigen Fassaden

FENSTER
- Pfosten-Riegel-Fassade Holz-Alu-Konstruktion in Schallschutzausführung zur Rheinstrasse
- Sonnenschutz als Horizontaljalousie

INNENWAND
- Sichtbeton in Fluren
- Trockenbauwände gestrichen
- Holzakustikverkleidung im Foyer, Türen integriert

HAUPTZUGANG
- Pfosten-Riegel-Fassade mit eingesetztem Türelement in Holz
- Holzverkleidung im Windfang

TIEFGARAGE
- Beschichtung auf Bodenplatte nach statischer Notwendigkeit
- unterseitige Dämmung der Geschossdecke EG

SOCKELZONE
- großformatige Betonwerksteinverkleidung
- Glasbrüstung zur Absturzsicherung

FASSADENAUSSCHNITT 1|50

